


PARAMBU — SOAP, OIL, FACEPACK & POWDER

FLOOR PLAN 36'-0" × 70'-0" = 2,520 SQ FT · EAST FACING

W1-W4 joined as soap · E-S is oil · north band joins raw material to W1 (no 4' path) · 2" panels · no false ceiling

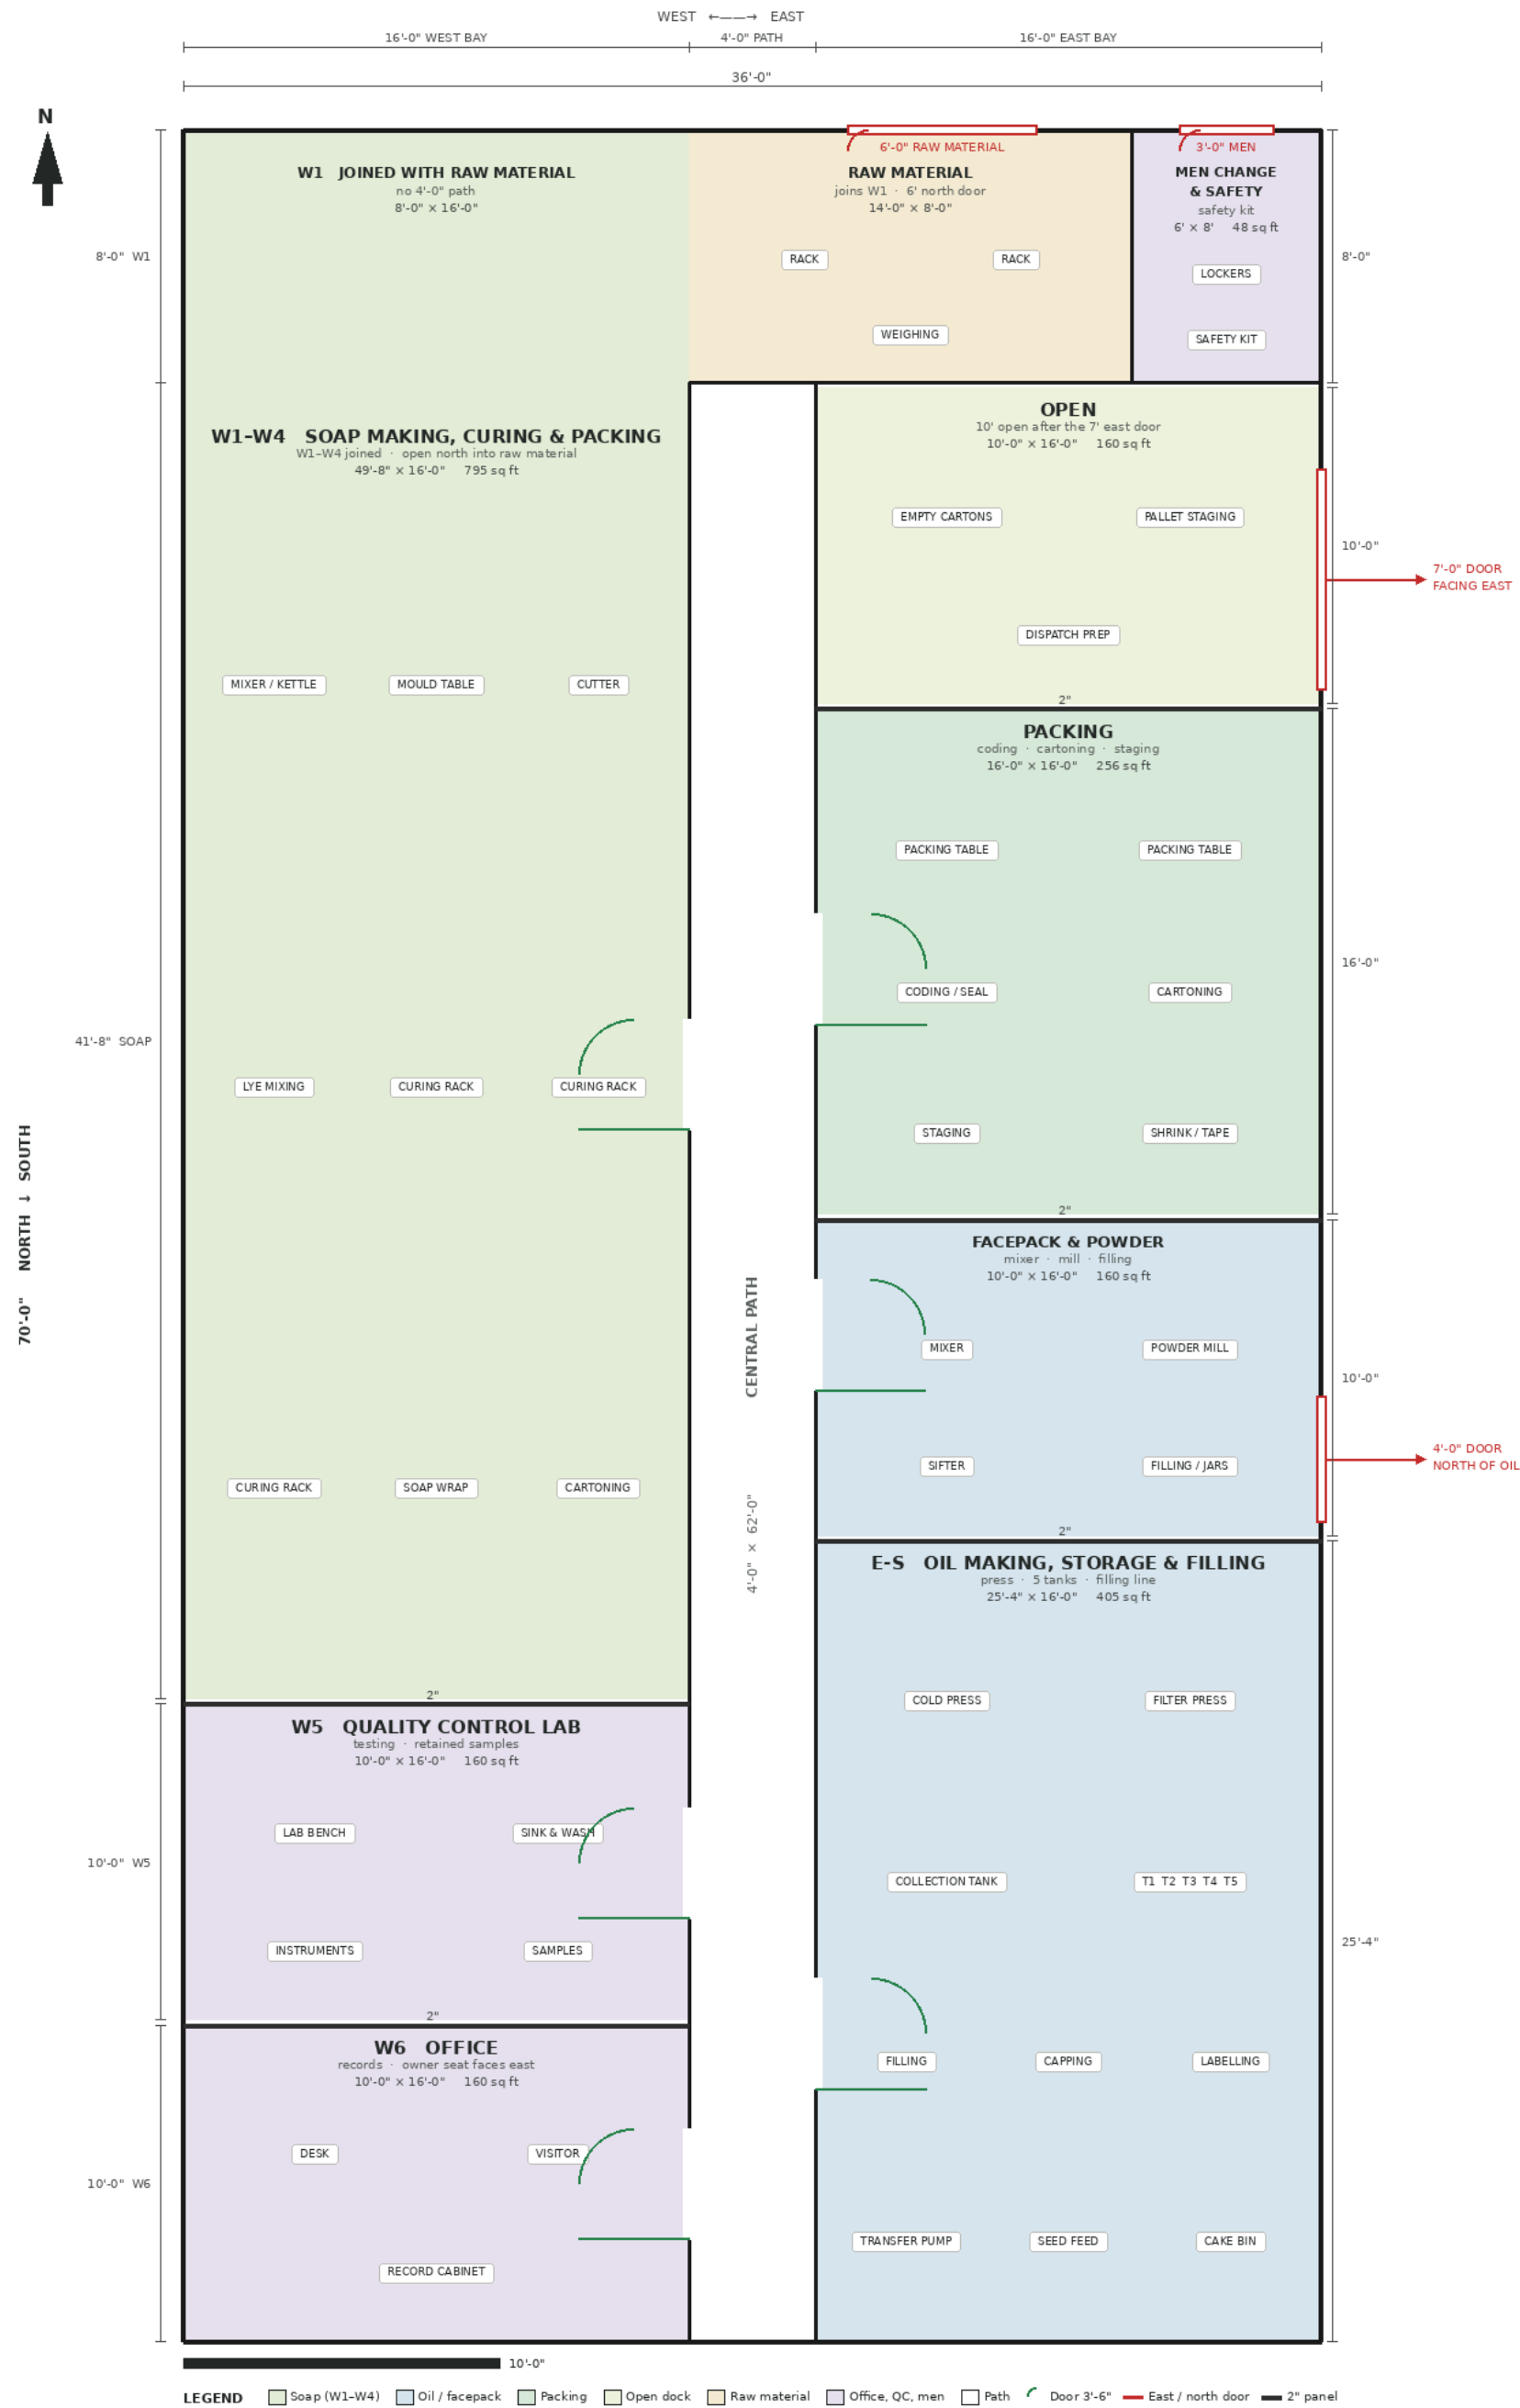

CONSTRUCTION NOTES

- W1, W2, W3 and W4 are one soap section (making, curing and packing). W5 is the QC lab. W6 is the office, south-west, owner seated facing east.
- The north 8'-0" band has no 4'-0" path. W1 is open to the raw-material room (E-N). Together they run 30'-0" to the men-change wall.
- E-N is divided: north-east 6'-0" x 8'-0" men change & safety kit, entered by a 3'-0" north door; the rest is the raw-material room, entered by a 6'-0" north door.
- E-S is oil making, storage and filling. Immediately north of it: a 4'-0" east door, then facepack & powder 10'-0" x 16'-0" (160 sq ft), then packing 16'-0" x 16'-0".
- A 7'-0" east door, just north of packing, opens into 10'-0" of open dock. Closed rooms use 2" (50 mm) panels. Soap is open to W1 — no panel there.
- East-west below the north band: 16'-0" west bay + 4'-0" path + 16'-0" east bay = 36'-0". Every production bay is 16'-0" deep.
- Floor: PVC mat, wood finish, over the full 36' x 70' shed. No false ceiling — roof structure left exposed, 12'-0" clear to purlins.
- Dimension check · west: 10 + 2" + 10 + 2" + 41'-8" + 8 = 70'-0" · east: 25'-4" + 2" + 10 + 2" + 16 + 2" + 10 + 2" + 8 = 70'-0".

PARAMBU — ROOM SCHEDULE

36'-0" × 70'-0" = 2,520 sq ft · east facing · W1–W4 joined soap · E-S oil

CODE	ROOM	SIZE	AREA	NOTES
W1–W4	Soap making, curing & packing	49'-8" × 16'-0"	795 sq ft	W1–W4 one room; W1 open to raw material
W1 / E-N	Raw material joined to W1	30'-0" × 8'-0"	240 sq ft	No 4' path; includes W1; 6'-0" north door
E-N	Men change & safety	6'-0" × 8'-0"	48 sq ft	North-east; 3'-0" north door
W5	Quality control lab	10'-0" × 16'-0"	160 sq ft	Bench, sink, retained samples
W6	Office	10'-0" × 16'-0"	160 sq ft	South-west; owner faces east
E-S	Oil making, storage & filling	25'-4" × 16'-0"	405 sq ft	Press, five tanks, filling line
—	Facepack & powder	10'-0" × 16'-0"	160 sq ft	North of the 4'-0" door
—	Packing	16'-0" × 16'-0"	256 sq ft	North of facepack
—	Open dock	10'-0" × 16'-0"	160 sq ft	Entered by the 7'-0" east door
P1	Central path	4'-0" × 62'-0"	248 sq ft	Stops at the north band

The 30' × 8' north band includes W1. Do not add it on top of the 795 sq ft soap hall.

DOORS

4'-0" east door — immediately north of oil (E-S), at the facepack room.
7'-0" east door — immediately north of packing; opens into the 10'-0" open dock.
3'-0" north door — men entry into the 6'-0" × 8'-0" change & safety room.
6'-0" north door — raw-material entry into E-N, which is open to W1.
Closed rooms (office, QC, soap, oil, facepack, packing) have 3'-6" doors to the path.
Floor: PVC mat, wood finish. Ceiling: none. Clear height 12'-0" to purlins.